ГУИР.6-05-0611-05.218 Э3

Блок внешний. Схема электрическая принципиальная

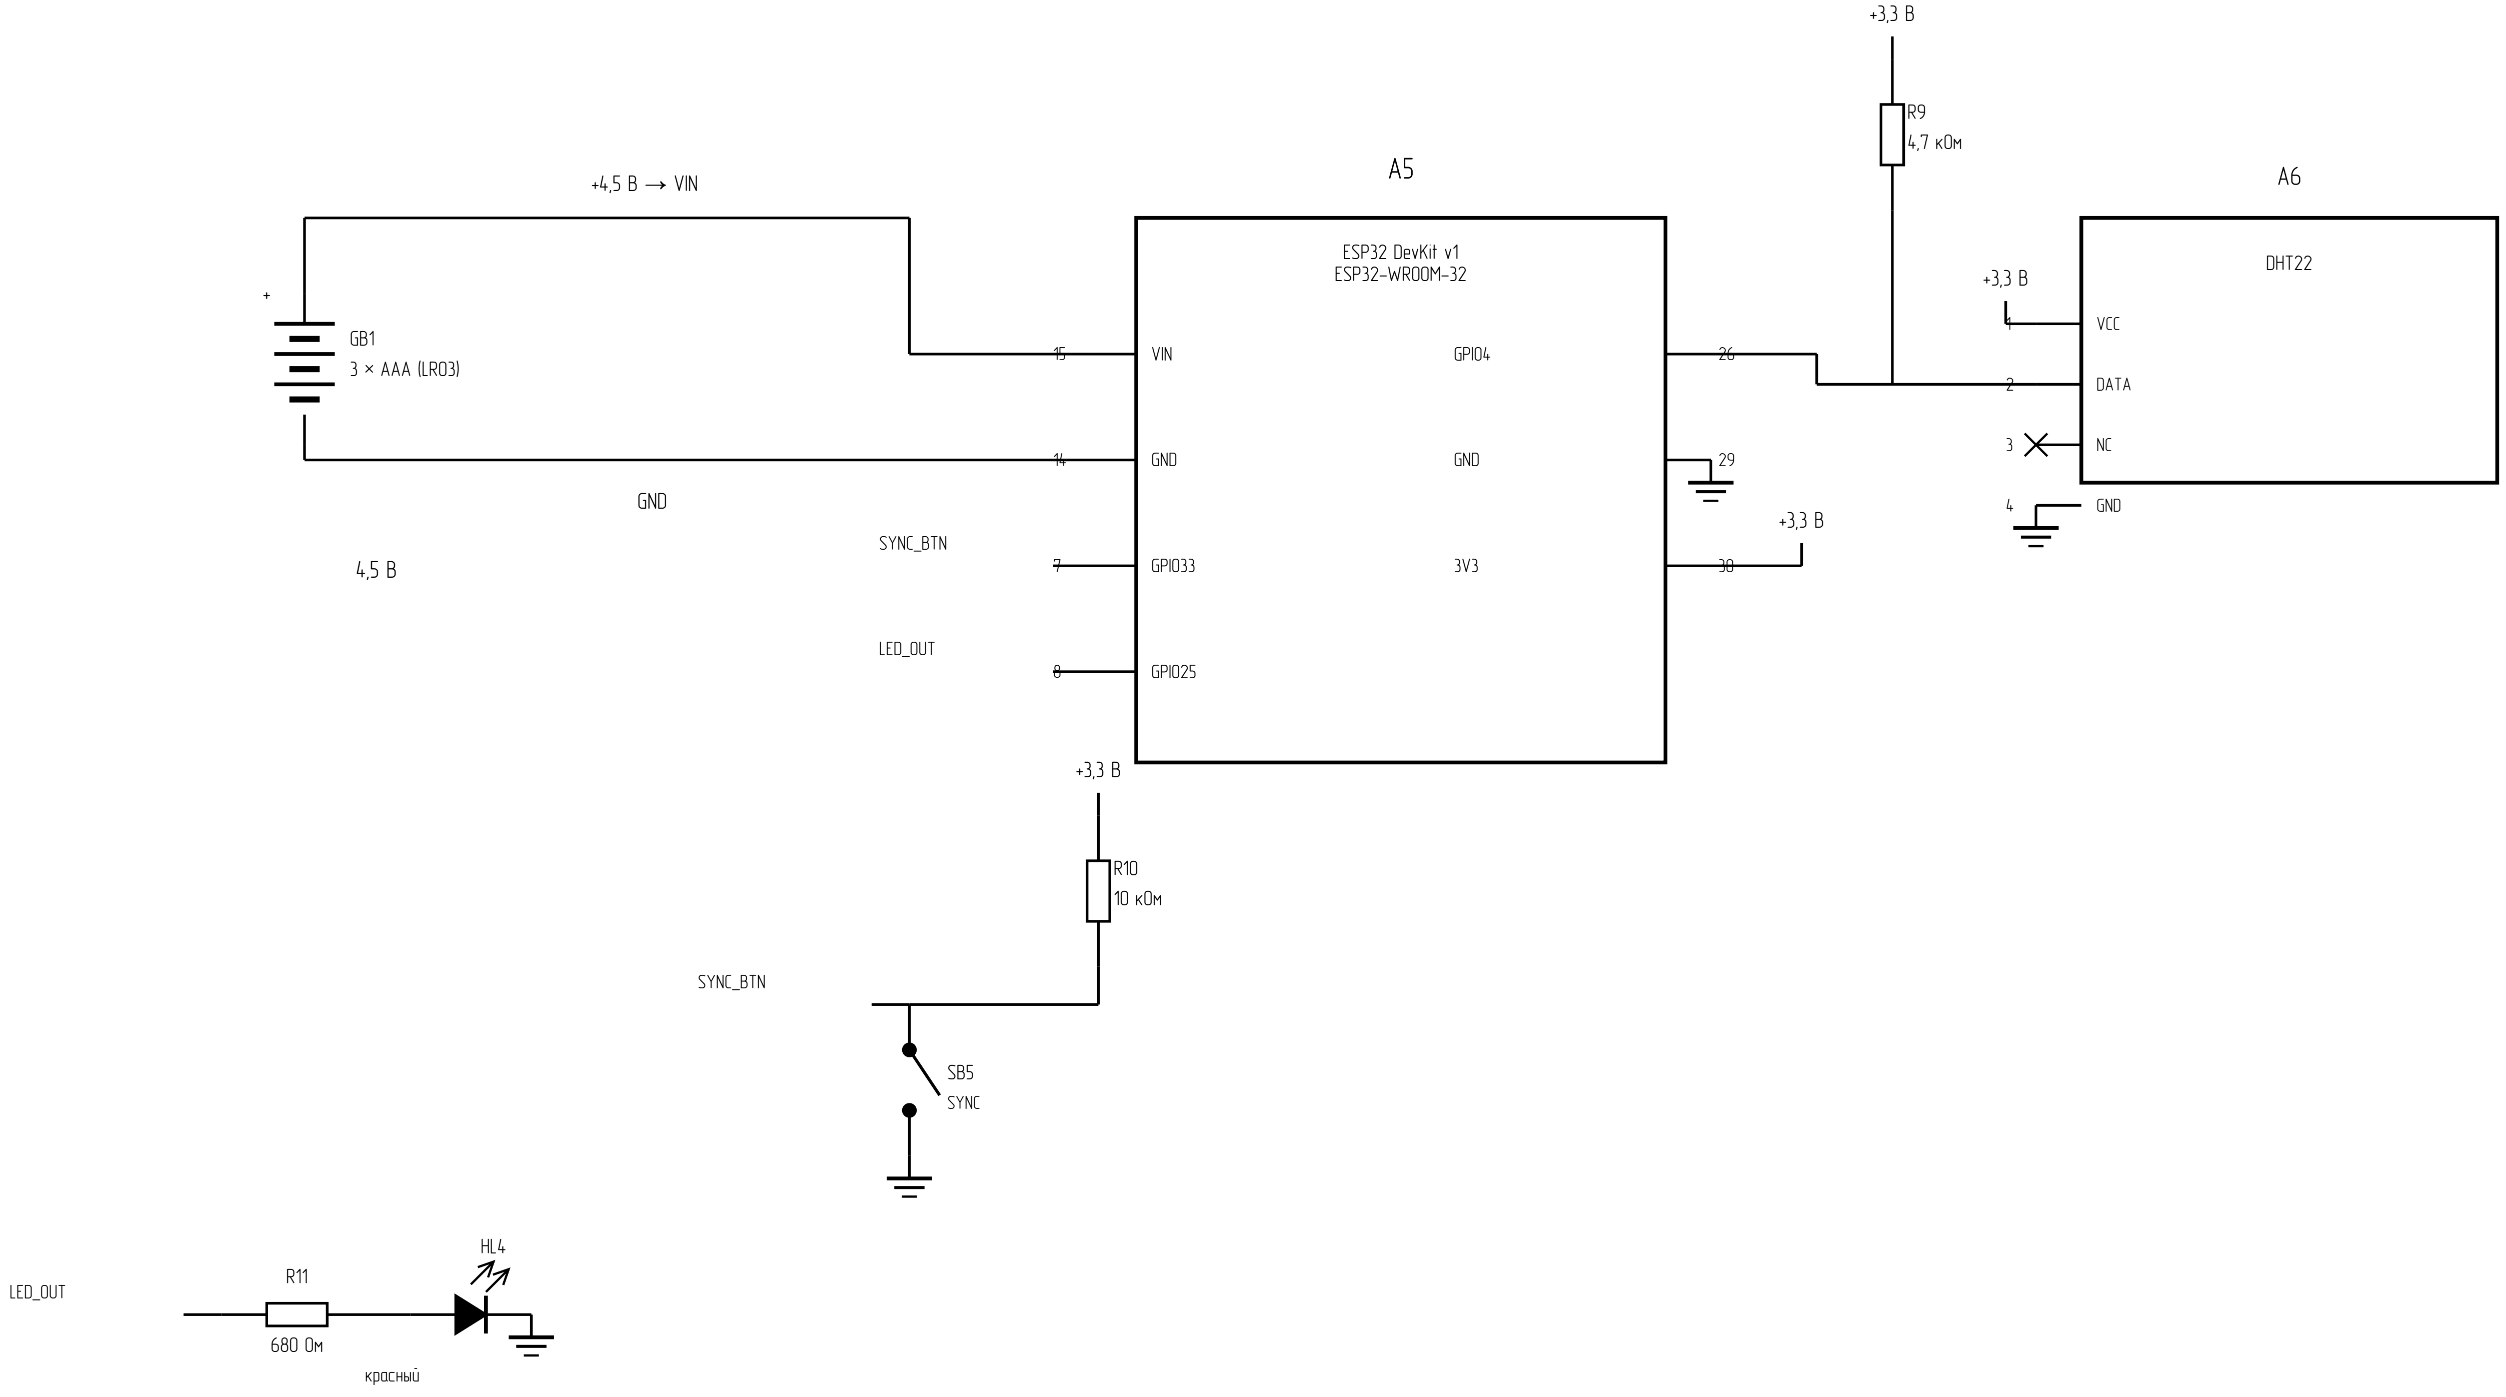

GB1 — три щелочные батарейки AAA (LR03), соединённые последовательно; номинал 4,5 В.

Плюс GB1 подключён к VIN (15), минус — к GND (14, 29). Внешний преобразователь отсутствует.

A5 — ESP32 DevKit v1 с ESP32-WROOM-32; его штатный стабилизатор формирует 3,3 В.

SB5 запускает внеочередное измерение и BLE-передачу. GPIO26 внешней схемой не используется.

ГУИР.6-05-0611-05.218 Э3

Разраб. Муравьёв
Пров. Стракович
Т. Контр.
Реценз.
Н. Контр.
Утв.

Метеостанция с выносным
уличным блоком.
Схема электрическая
принципиальная

1
2

ЭВМ, гр. 450502

ГУИР.6-05-0611-05.218 Э3

Блок комнатный. Схема электрическая принципиальная

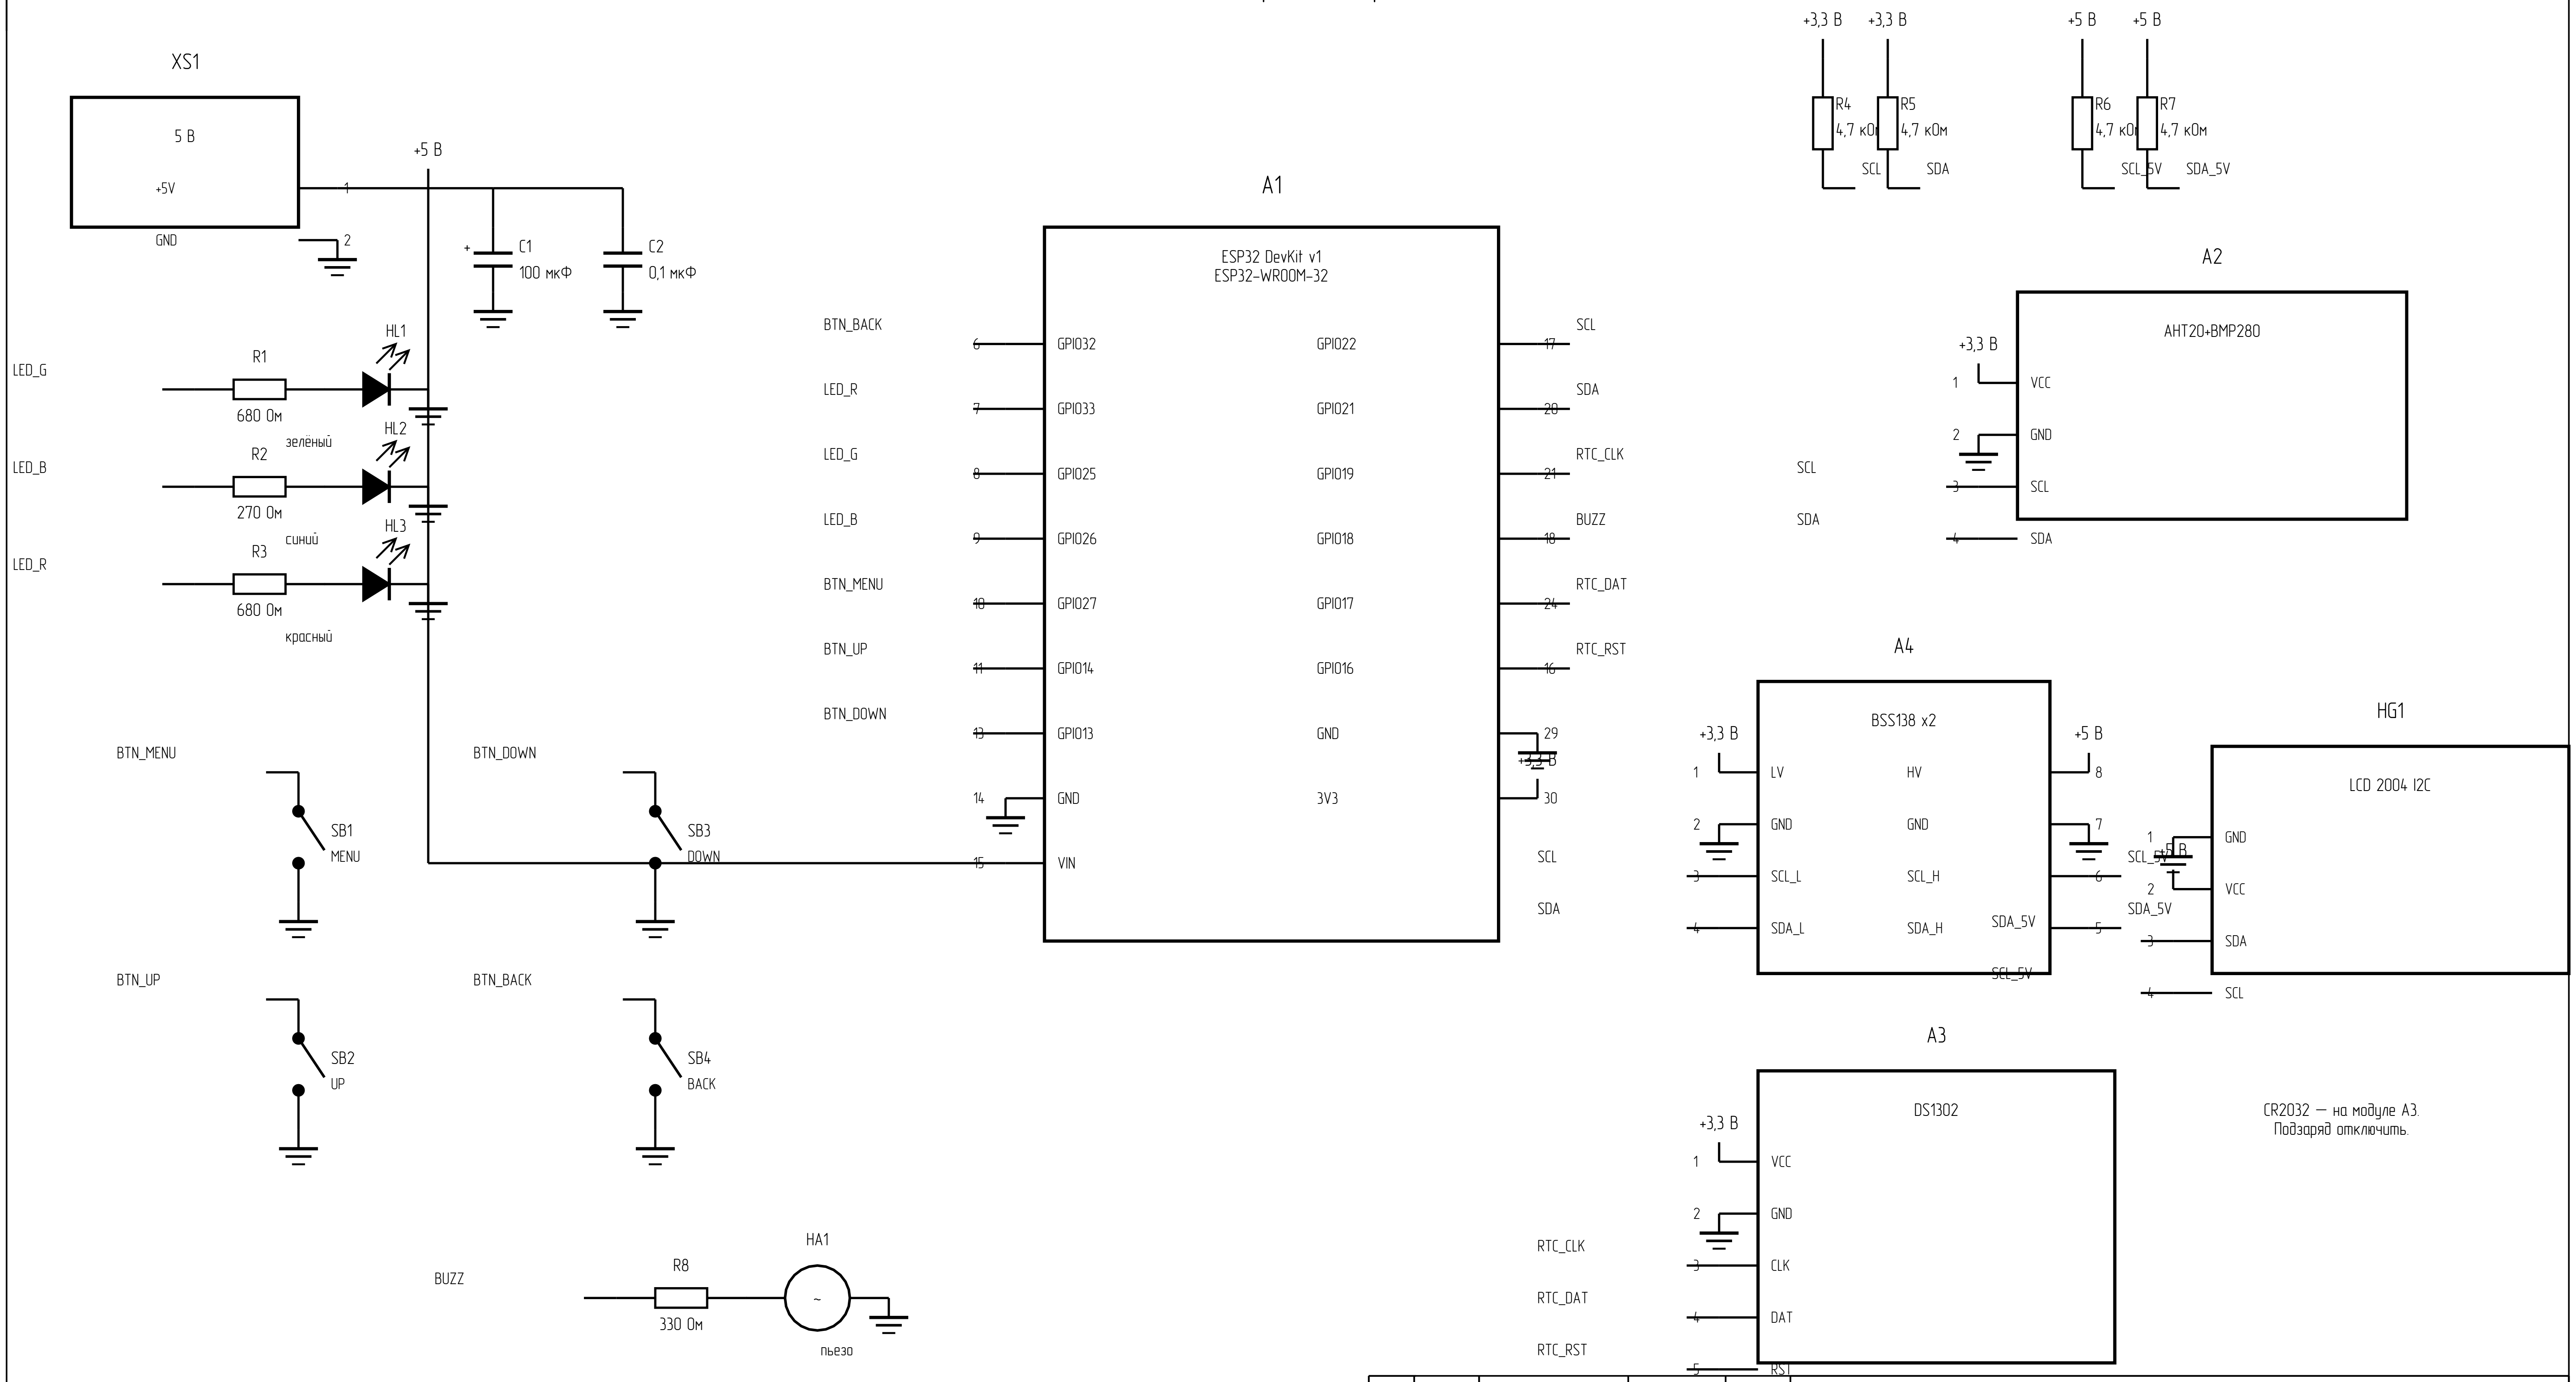

Примечания. A1 — плата ESP32 DevKit v1; показаны используемые выводы. Питание 5 В — через XS1 или USB.

HG1 питается от 5 В, связь с A1 — через A4. Адреса: AHT20 0x38, BMP280 0x76, PCF8574 0x27/0x3F.

Кнопки SB1–SB4 замыкают GPIO на GND, подтяжка внутренняя. HA1 — пассивный пьезоизлучатель.

За основу принят EasyEDA-файл внутреннего блока; добавлены A4, R4–R7 и уточнены номиналы R1–R3.

ГУИР.6-05-0611-05.218 Э3

Метеостанция с выносным уличным блоком.

Схема электрическая принципиальная

Разраб. Муравьёв
Пров. Стракович
Т. Контр.
Реценз.
Н. Контр.
Утв.

2
2

ЭВМ, гр. 450502