
ГУИР.6-05-0611-05.218 Э2

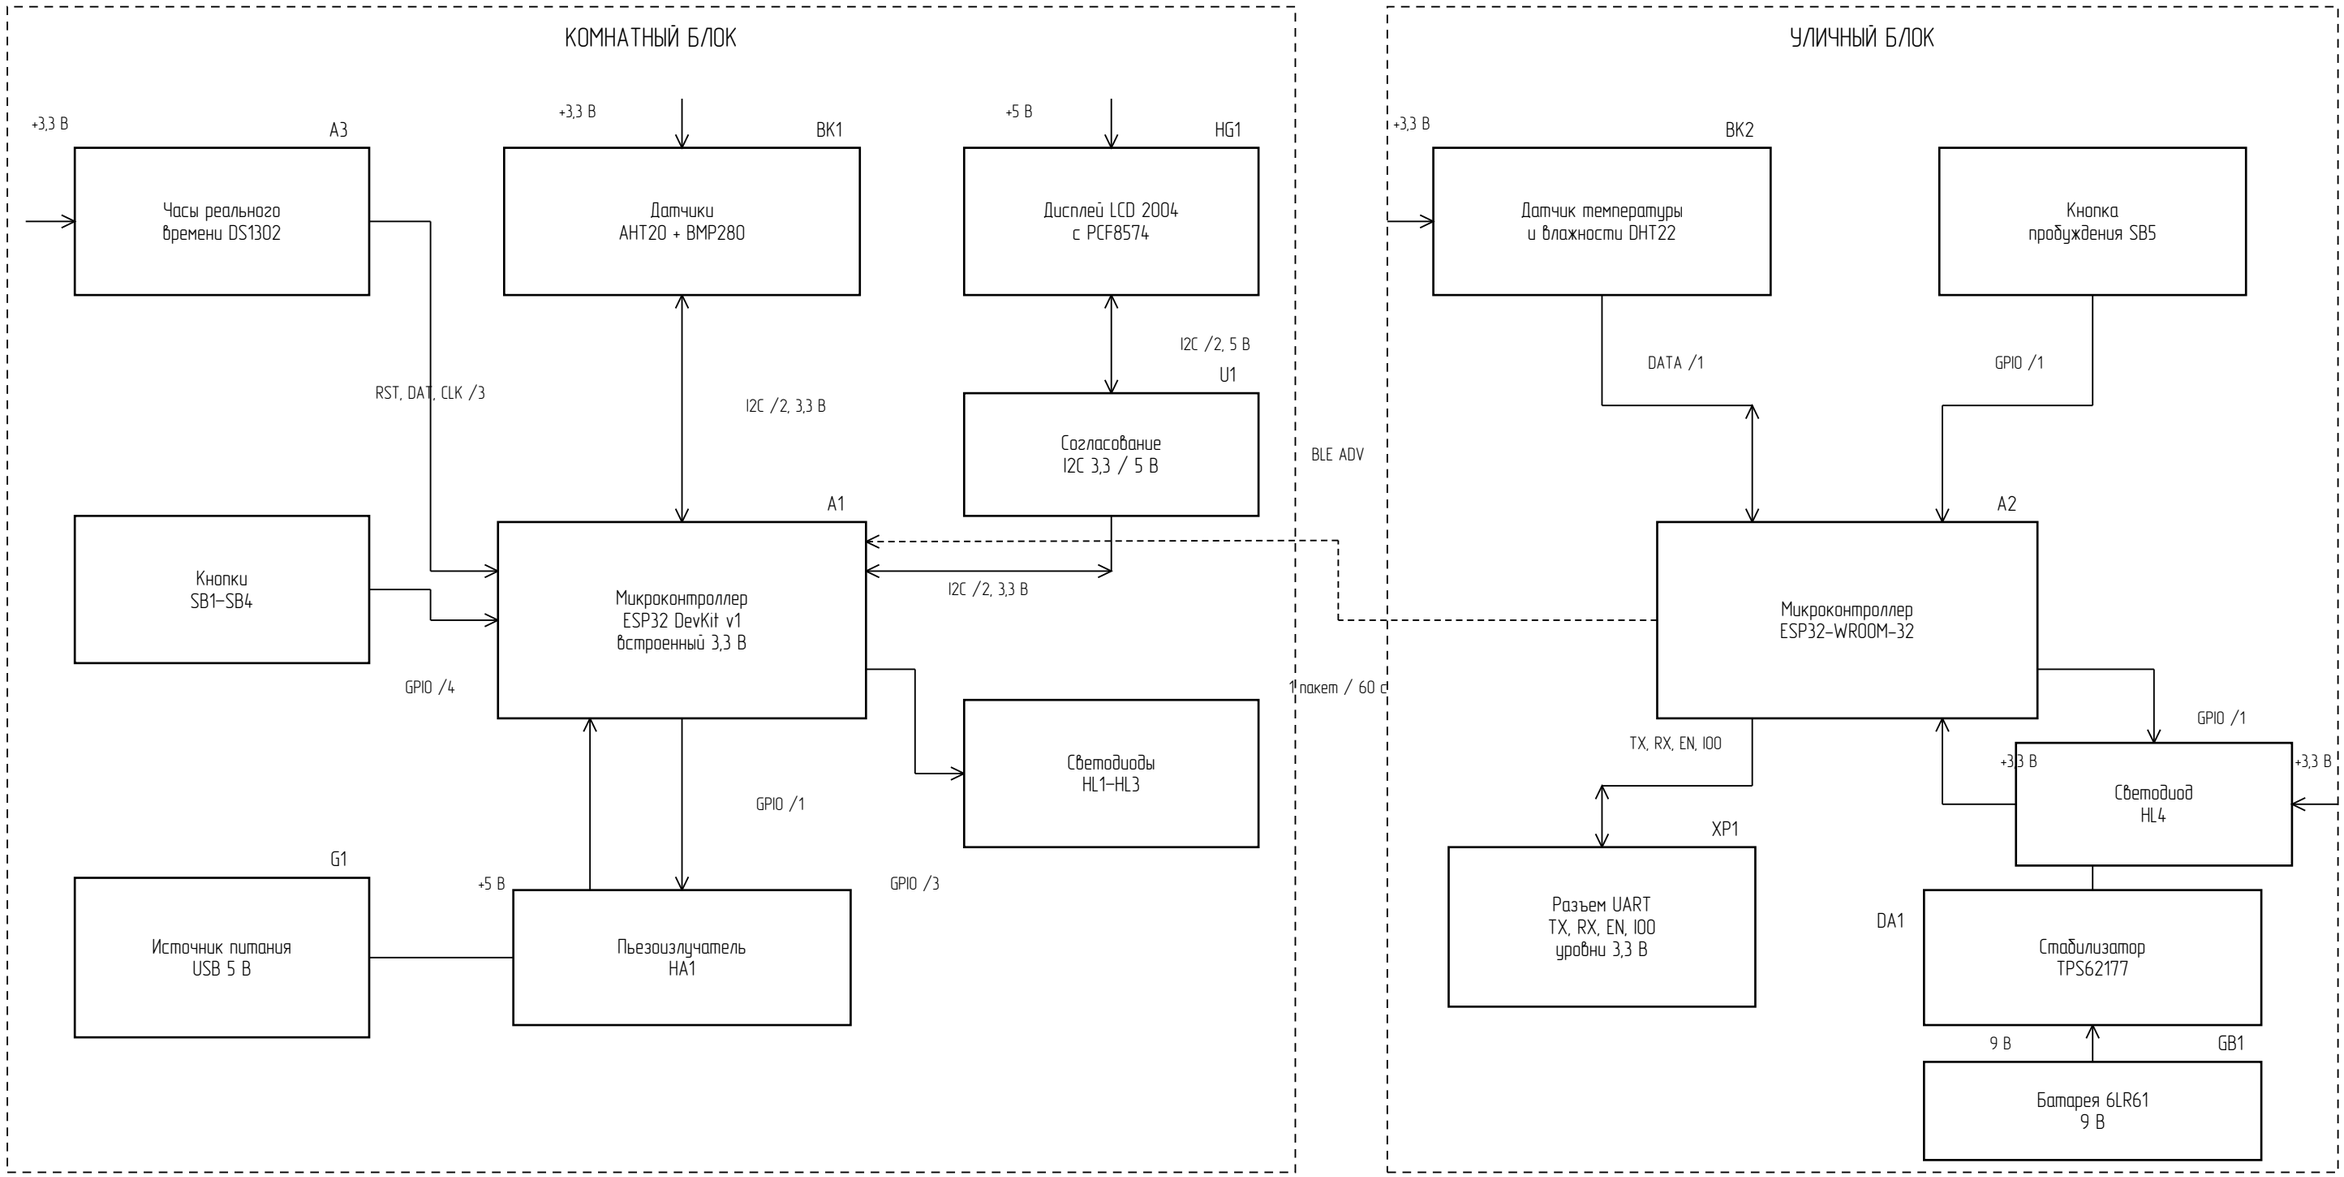

Сплошные линии — сигнальные связи; пунктир — радиоканал BLE.

Короткие стрелки — питание; одинаковые обозначения шин соединены электрически.

GND каждого блока — общий провод его схемы. Число после «/» — количество сигнальных линий.

					ГУИР.6-05-0611-05.218 Э2	
						Лит. / Масса / Масштаб
Изм.	Лист	№ докум.	Подп.	Дата	Метеостанция с выносным уличным блоком. Схема электрическая функциональная	Т
Разраб.		Муравьёв				Лист / Листов: 1
Пров.		Страковичч				
Т. Контр.						ЭВМ, гр. 450502
Реценз.						
Н. Контр.						
Утв.						